




- FRONT ELEVATION

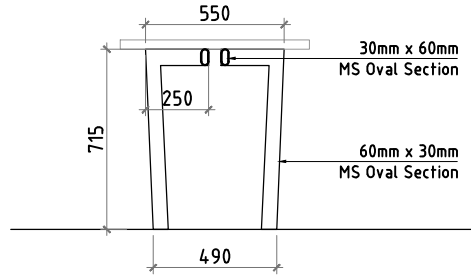


- FRONT SECTIONAL ELEVATION

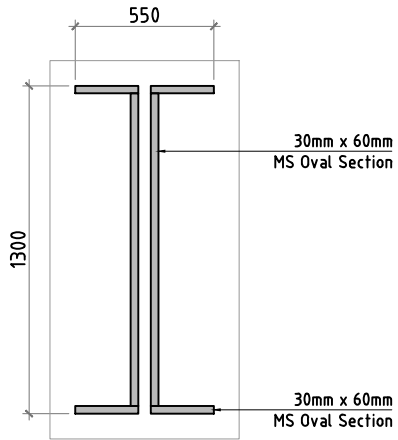

- TOP PLAN @ 750MM LVL.

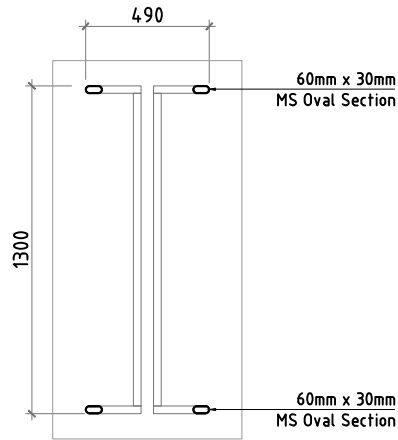

- PLAN @ 300MM LVL.

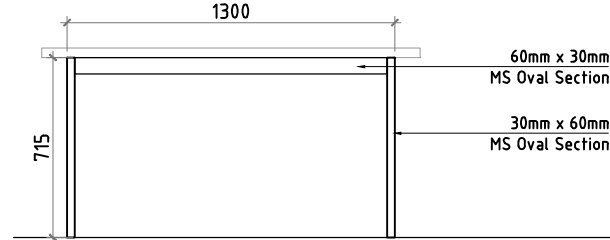

- SIDE SECTIONAL ELEVATION

Drawing Title	Shweta's Table
Drawing Number	I-502
Revision Number	Dealt/Checked AJ / CK
Scale nts @ A4	Orientation
Date 30.12.2019	
Drawing Status Concept	

Notes

1. All dimensions as in millimeters unless otherwise mentioned.
2. Do not scale this drawing - follow only written dimensions.
3. In case of any discrepancies, notify the architect immediately, before commencement of work.
4. This drawing and all written content herein, is the property of TheseThings.Co. No part of this drawing may be reproduced, used or disclosed in any manner whatsoever without the express written consent of the Architect.

SECTION USED :
Oval MS Section 30mm x 60mm
2.5mm thickness minimum

Finish : Rust / Clear Powdercoat

QUANTITY = 3 Nos.

01	First release	AJ	30.12.19
Rev.	Description	Dealt by	Date

Client Name SEEMA KAPOOR

Project Number TT_08

Project Title 431-88 STUDIO

THESETHINGS.CO

BD 14H, Top Floor, DDA Flats,
Munirka
New Delhi -110067