

- Notes
1. All dimensions as in millimeters unless otherwise mentioned.
 2. Do not scale this drawing - follow only written dimensions.
 3. In case of any discrepancies, notify the architect immediately, before commencement of work.
 4. This drawing and all written content herein, is the property of TheseThings.Co. No part of this drawing may be reproduced, used or disclosed in any manner whatsoever without the express written consent of the Architect.

1200

600

SIZE OF PANEL : 1200MM X 600MM

TIMBER BATTON : 50MM

FULL LENGTH

NO.S OF PANEL : 44

01	First release	AJ	07.06.20
Rev.	Description	Dealt by	Date


Client Name SEEMA KAPOOR

Project Number TT_08


Project Title 431-88 STUDIO

THESETHINGS.CO

BD 14H, Top Floor, DDA Flats,
Munirka
New Delhi -110067

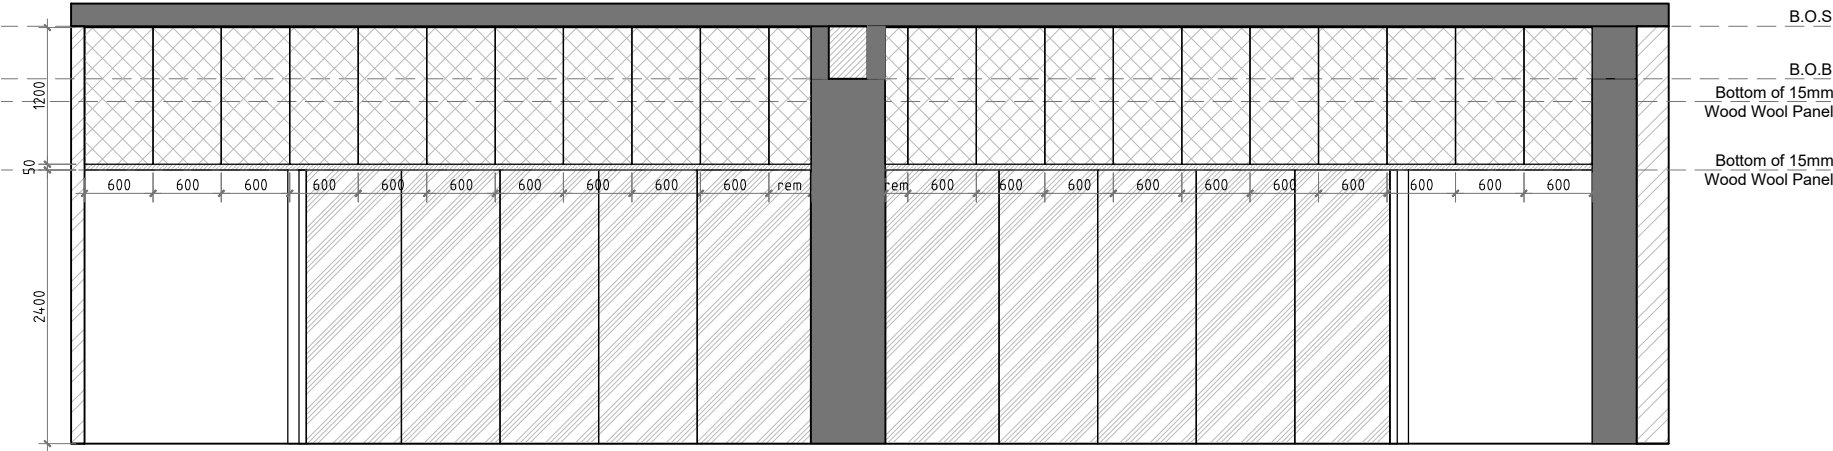

Side A

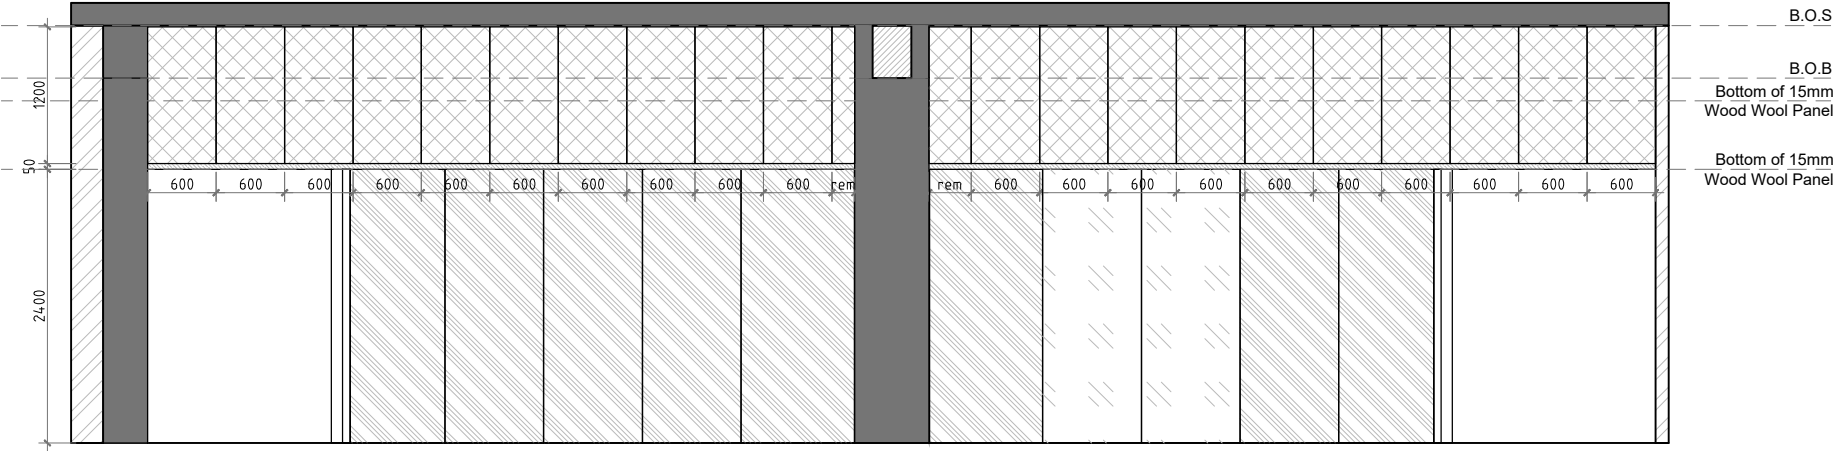

Side C