


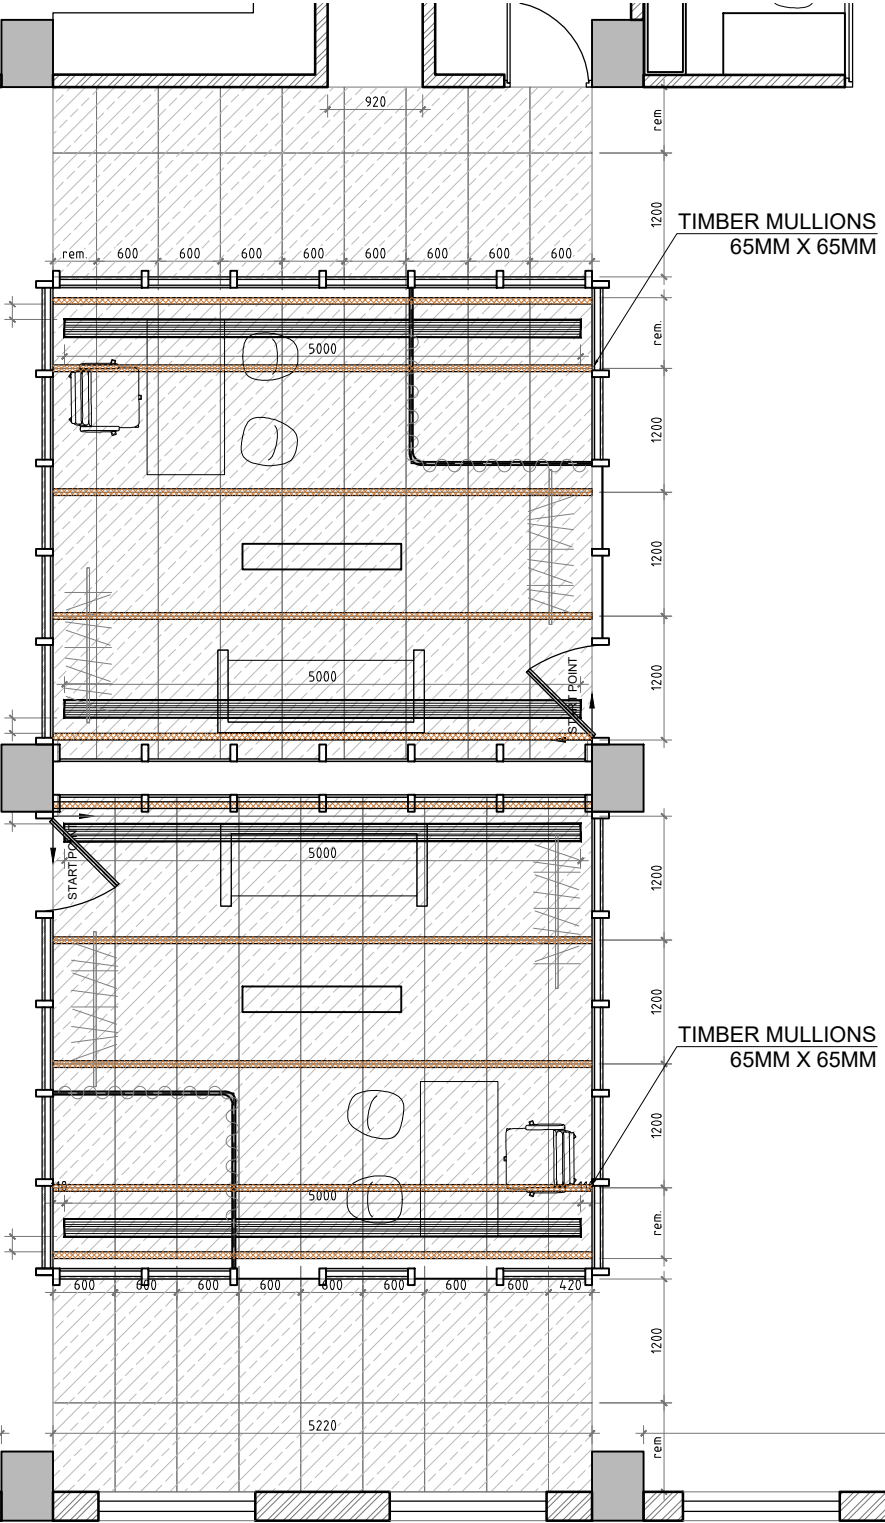

Drawing Title
Meeting Room Layout Plan

Drawing Number
I-104

Revision Number
Dealt/Checked
AJ / CK


Scale
nts@ A4

Date
07.06.2020

Drawing Status
Concept

Notes

1. All dimensions as in millimeters unless otherwise mentioned.
2. Do not scale this drawing - follow only written dimensions.
3. In case of any discrepancies, notify the architect immediately, before commencement of work.
4. This drawing and all written content herein, is the property of TheseThings.Co. No part of this drawing may be reproduced, used or disclosed in any manner whatsoever without the express written consent of the Architect.

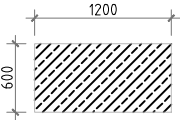

SIZE OF PANEL : 1200MM X 600MM
TIMBER MULLIONS : 65MM X 165MM
NO.S OF PANEL : 108

02	Update	AJ	07.06.20
01	First release	AJ	04.06.20
Rev.	Description	Dealt by	Date

Client Name
SEEMA KAPOOR

Project Number
TT_08

Project Title
431-88 STUDIO

THESETHINGS.CO

BD 14H, Top Floor, DDA Flats,
Munirka
New Delhi -110067