


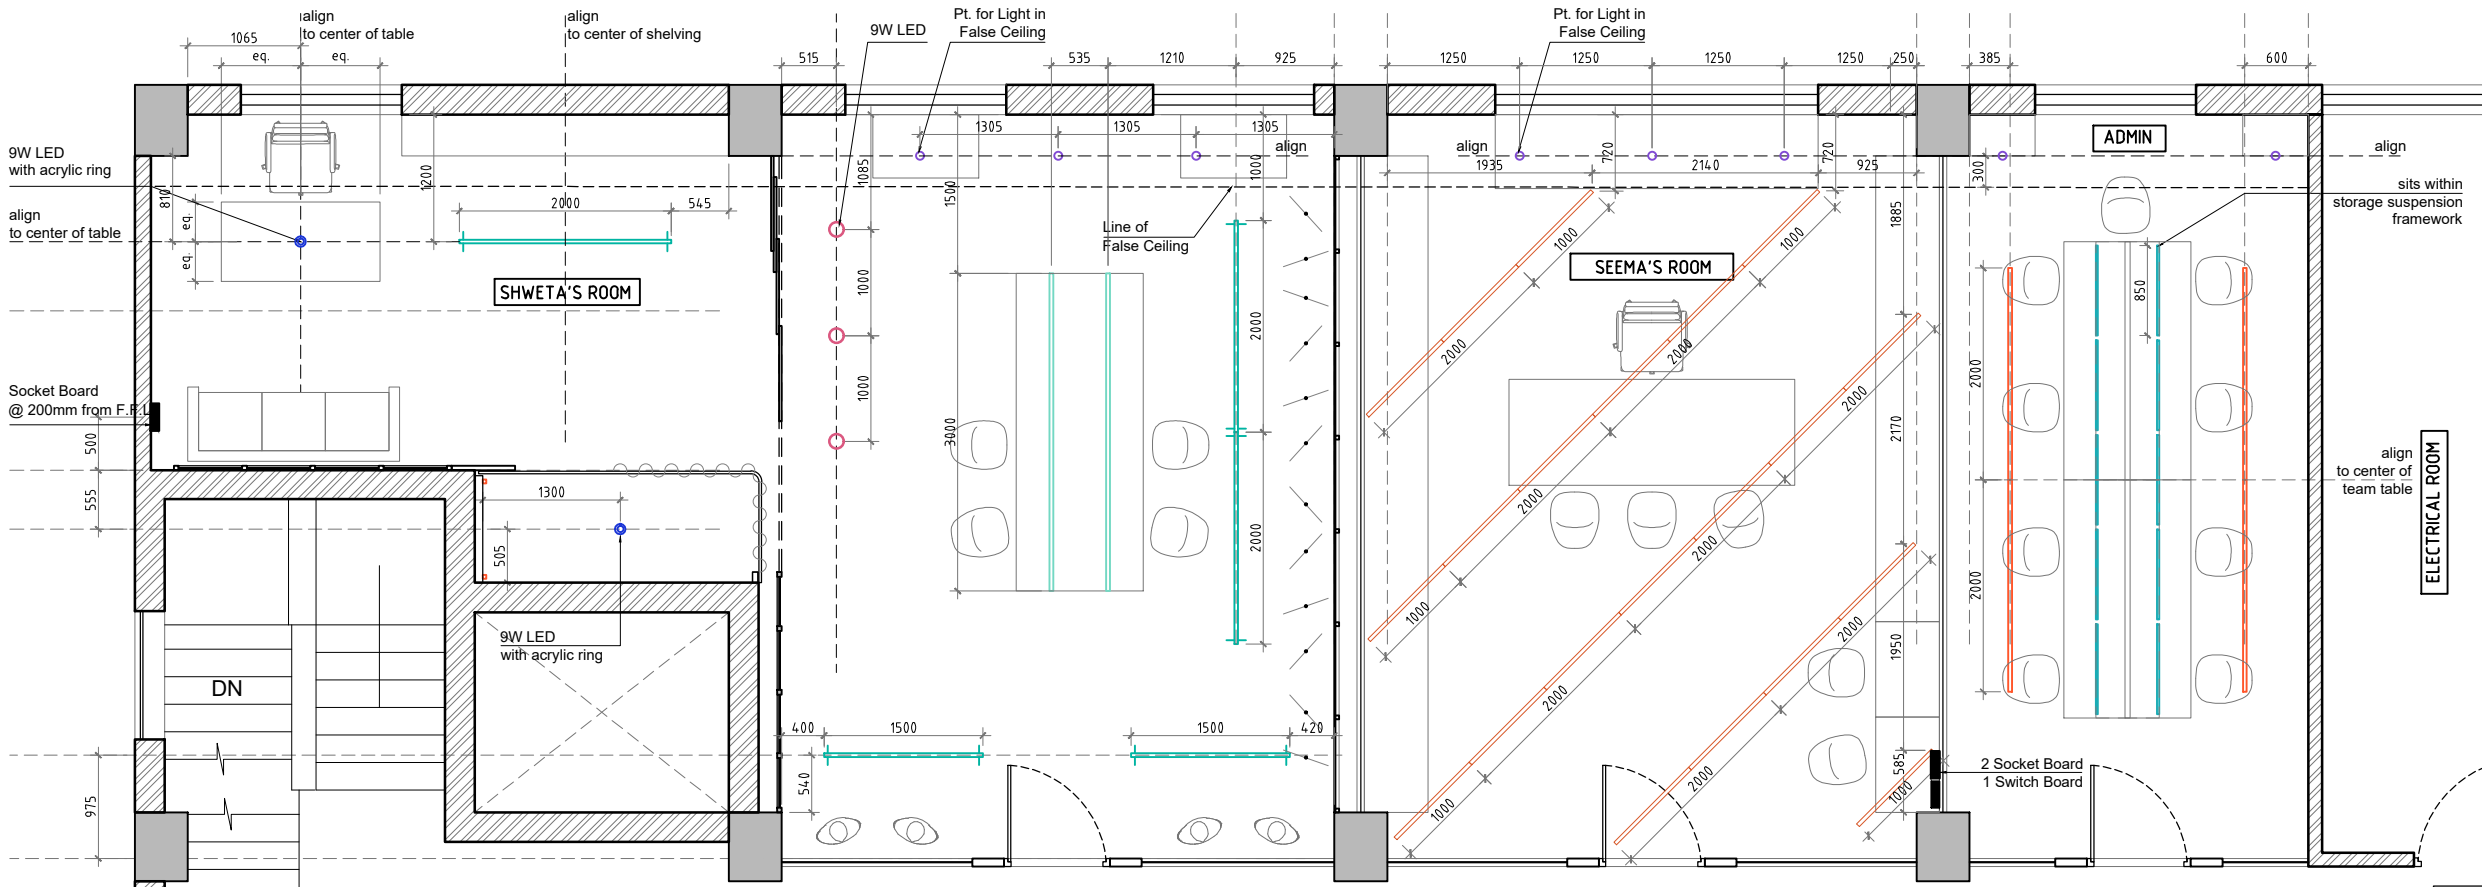

Drawing Title
Lighting Layout Plan

Drawing Number
I-121

Revision Number
3

Dealt/Checked
AJ / CK

Scale
1:100 @ A3

Orientation

Date
18.06.2020

Drawing Status

- Notes
1. All dimensions as in millimeters unless otherwise mentioned.
 2. Do not scale this drawing - follow only written dimensions.
 3. In case of any discrepancies, notify the architect immediately, before commencement of work.
 4. This drawing and all written content herein, is the property of thesethings.co. No part of this drawing may be reproduced, used or disclosed in any manner whatsoever without the express written consent of the Architect.

LEGEND			
S.No.	Symbol	Fixture Name	Quantity
1		9 W Down Light with Acrylic and Brass / 3000K	10
2		2m Linear Light / 4000K	12
3		LED Strip in Aluminum U-Section / 850mm length / 3000K	10
4		9 W Down Light without Acrylic / 3000K	3
5		1m Linear Light / 4000K	5
6		2m Track with Spot (as specified)	5
7		1.5 m Track with Spot	6
8		3000mm Linear Light/ Suspended/ 3000K	1
9		Vertical Mirror Light 2m / 3000K	6
10		12W Track Spot/ 4000K	24

01 First release AJ 16.06.20

Rev. Description Dealt by Date

Client Name 431-88

Project Number TT_08

Project Title 431-88 STUDIO

thesethings.co

BD 14H, Top Floor, DDA Flats,
Munirka
New Delhi -110067